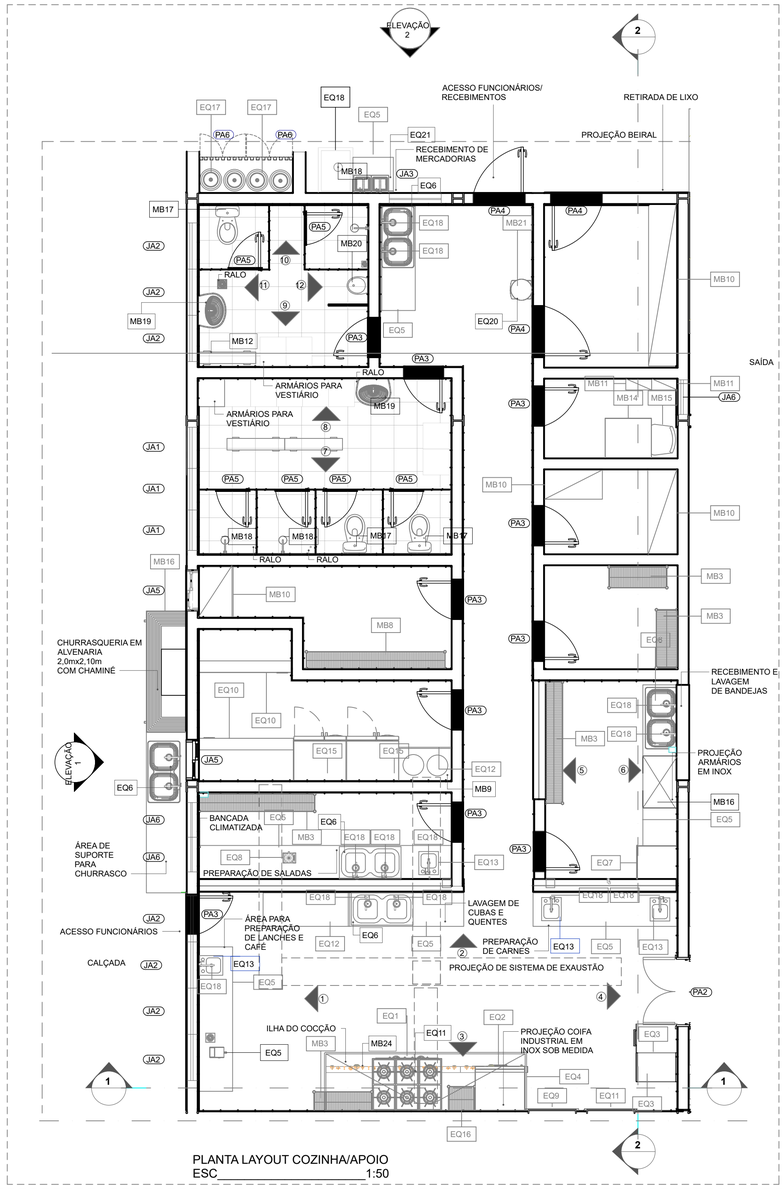

PLANTA LAYOUT COZINHA/APOIO
ESC_____1:50

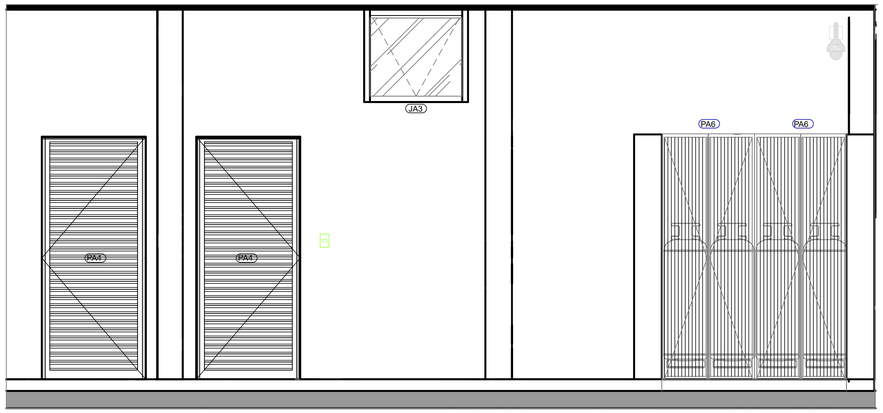

ESQUADRIAS FACHADA DIANTEIRA (2) - COZINHA/APOIO
ESC_____1:25

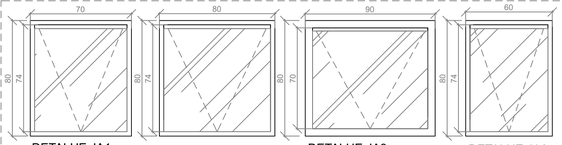

DETALHE JA1
ESC_____1:20

DETALHE JA2
ESC_____1:20

DETALHE JA3
ESC_____1:20

DETALHE JA6
ESC_____1:20

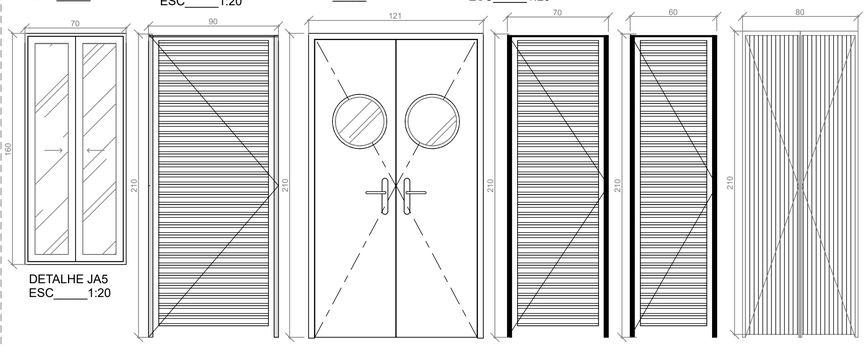

DETALHE JA5
ESC_____1:20

DETALHE PA4
ESC_____1:20

DETALHE PA2
ESC_____1:20

DETALHE PA3
ESC_____1:20

DETALHE PA2
ESC_____1:20

DETALHE PA6
ESC_____1:20

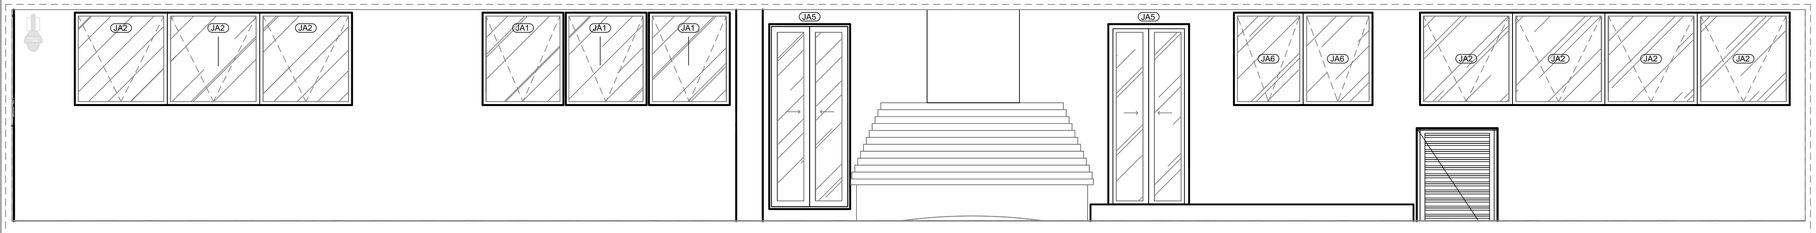

ESQUADRIAS FACHADA LATERAL (1) - COZINHA/APOIO
ESC_____1:25

MAPA CHAVE

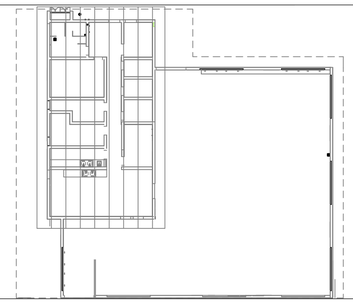

LEGENDA

TABELA DE EQUIPAMENTOS E MOBILIARIOS APOIO

Legenda	Descrição	Contagem
EQ1	FOGÃO INDUSTRIAL 6 BOCAS 40X40 PREMIUM METALMARQ OU SIMILAR	1
EQ2	FORNO INDUSTRIAL COM MENU DIGITAL RATIONAL SCC 101 MODELO ELÉTRICO 84x77x104cm	1
EQ3	CARRO CARRINHO 3 BANDEJAS AÇO INOX PARA REFEITÓRIO COM RODAS RICHOA OU SIMILAR	2
EQ4	COIFA INDUSTRIAL SOB MEDIDA 350X80CM EM INOX MONTADAS E FORNECIDAS PELA IMPERIAL CALHAS OU LOJA SIMILAR	1
EQ5	<varia>	10
EQ6	CUBA DE INOX INDUSTRIAL DUPLA ACETINADA TRAMONTINA ISIS 2C 34-28 BS PROFUNDIDADE 14cm OU SIMILAR	5
EQ7	MÁQUINA DE LAVAR LOUÇAS 14 SERVIÇOS EM AÇO INOX 127V OU 220V BRASTEMP OU SIMILAR	1
EQ8	LIQUIDIFICADOR INDUSTRIAL BAIXA ROTAÇÃO LQL 368W 8L METVISA 220V PRATA OU SIMILAR	1
EQ9	PASSTROUGH AQUECIDO E RESFRIADO 600 TEMP MÁX 60C POR RESISTÊNCIA ELÉTRICA COM CONTROLADOR DIGITAL LINHA REFRIMATE OU SIMILAR	1
EQ10	FREEZER HORIZONTAL 2 PORTAL 534L 220V CONSUL OU SIMILAR	2
EQ11	PASSTROUGH AQUECIDO E RESFRIADO 600 TEMP MÁX 60C POR RESISTÊNCIA ELÉTRICA COM CONTROLADOR DIGITAL LINHA REFRIMATE OU SIMILAR	1
EQ12	MESA INOX TAMPO ESPELHO TRASEIRO E BORDA QUEBRA ÁGUA PRATELEIRA TUBULAR ESCOVADO COM PÉS EM TUBO INOX SEM ABERTURAS OU LISA 870 A 2870 SOB MEDIDA MONTADAS E FORNECIDAS PELA MISTERINOX OU SIMILAR	2
EQ13	TTRAMONTINA 94020/102 CUBA LAVÍNIA EM AÇO INOX ACETINADO, 40X34 CM, PRATA	4
EQ15	REFRIGERADOR VERTICAL COM PORTAS BIPARTIDAS 02 OU 04 PORTAS COZIL OU SIMILAR	2
EQ16	ESTANTE DE APOIO PARA FORNO E PÃO INDUSTRIAL 170X45X45cm EM PERFIL INOX COM ACABAMENTO ESCOVADO E ESPAÇO PARA BANDEJAS 8cm PRAKASA METAIS OU SIMILAR	1
EQ17	GAS CILINDRO - LPG - 45kg (88 LITROS)	4
EQ18	TORNEIRA PARA PIA DE COZINHA INDUSTRIAL GALI METAL BICA ALTA DOCOL OU SIMILAR	22
MB6	MESA EM AÇO INOX TAMPO SUPERIOR LISO ESCOVAMESA INOX TAMPO ESPELHO TRASEIRO E BORDA QUEBRA ÁGUA PRATELEIRA TUBULAR ESCOVADO COM PÉS EM TUBO INOX COM ABERTURA PARA CUBAS OU LISA 870 A 2870 SOB MEDIDA MONTADAS E FORNECIDAS PELA MISTERINOX OU SIMILAR	1
MB7	JARDINEIRA PARA PLANTAS FLOREIRA DE POLIETILENO HAVANA COR CINZA SOB MEDIDA MARCA ALPE&ARITANA OU SIMILAR	1
MB8	ESTANTE LISA OU PERFURADA DE SUPORTE EM AÇO INOX 150KG A 400KG POR PLANO PARA COZINHAS COZIL OU SIMILAR	1
MB9	TV SAMSUNG 32 POLEGADAS COM SUPORTE PARA PAREDE OU SIMILAR	5
MB10	ARMÁRIO MULTIUSO BRANCO PARA ÁREAS DE SERVIÇO/DML AR4000 ART IN MÓVEIS OU SIMILAR	4
MB11	ARMÁRIO MULTIUSO BRANCO PARA ESCRITÓRIOS COM PRATELEIRAS AJUSTÁVEIS 02 PORTAS CONTROLIV OU SIMILAR	2
MB12	BANCO PARA VESTIÁRIO ESTILO INDUSTRIAL MARROM DESIGNOFFICE OU SIMILAR	3
MB14	MESA PEQUENA AUXILIAR PARA ESCRITÓIO 80X70 MAXXI CINZA OU SIMILAR	1
MB15	CADEIRA PARA ESCRITÓRIO BASE CROMADA COM RODINHA FORTT LISBOA PRETA OU SIMILAR	1
MB16	CHURRASQUEIRA EM ALVENARIA FEITA SOB MEDIDA	1
MB21	BEBEDOURO BIV CAPACIDADE 10 OU 20L AQUAPLUS BRITÂNIA OU SIMILAR	1
MB22	MESA ESTILO INDUSTRIAL PEQUENA PARA CAFÉ 25x40x50cm MARCA LOVE PALLETS OU SIMILAR	1
TOTAL GERAL: 83		

NÍVEL TÉRREO REFEITÓRIO				
JA1	JANELA BASCULANTE PVC COM PUXADOR E CORRENTE PARA ABERTURA 1,5m PEITORIL 2,4m 70x80	70 cm	80 cm	3
JA2	JANELA BASCULANTE PVC COM PUXADOR E CORRENTE PARA ABERTURA 1,5m PEITORIL 2,4m 80x80	80 cm	80 cm	8
JA3	JANELA BASCULANTE PVC COM PUXADOR E CORRENTE PARA ABERTURA 1,5m PEITORIL 2,4m 90x80	90 cm	80 cm	1
JA4	JANELA DE CORRER 2 FOLHAS PVC 160X80 PEITORIL 1,40m	350 cm	160 cm	9
JA5	JANELA DE CORRER 2 FOLHAS PVC 120X70 PEITORIL 1,40m	70 cm	160 cm	2
JA6	JANELA BASCULANTE PVC COM PUXADOR E CORRENTE PARA ABERTURA 1,5m PEITORIL 2,4m 60x80	60 cm	80 cm	3
TOTAL GERAL: 26				26

NÍVEL TÉRREO REFEITÓRIO				
PA1	PORTA PRONTA DUPLA ENTRADA REFEITÓRIO BRANCA EM MADEIRA COM ENCHIMENTO SÓLIDO OU BONDOOR E FITA EM PVC NAS LATERAIS E SOLEIRA 240 x 210	241 cm	211 cm	2
PA2	PORTA VAI E VEM METAL RIB OU SIMILAR PARA TRÁFEGO ALTO COM ACABAMENTO EM CHAPA DE AÇO OU AÇO INOX120 x 210	121 cm	211 cm	1
PA5	PORTA VENEZIANA DE GIRO ALUMÍNIO BRANCO COM FECHADURA 2,10x0,60 LINHA HOME 3A OU SIMILAR	60 cm	210 cm	6
PA3	PORTA VENEZIANA DE GIRO ALUMÍNIO BRANCO COM FECHADURA 2,10x0,70 LINHA HOME 3A OU SIMILAR	70 cm	210 cm	10
PA4	PORTA VENEZIANA DE GIRO ALUMÍNIO BRANCO COM FECHADURA 2,10x0,90 LINHA HOME 3A OU SIMILAR	90 cm	210 cm	3
TOTAL GERAL: 22				22

PA6	PORTA GRADIL PARA CASA DE GÁS 40x210cm	40cm	210cm	4		

REV.	TE	DESCRIÇÃO	PROJ.	DES.	VER.	APR.	AUT.	DATA
2	H	CANCELADOS	FCG	FCG	MGT	FOJ	MMR	27/02/24
1	B	PARA APROVAÇÃO	FCG	FCG	MGT	FOJ	MMR	31/01/24
0	B	EMISSÃO INICIAL	FCG	FCG	MGT	FOJ	MMR	07/12/23

EMISSÕES

TE TIPO DE EMISSÃO
(A) PRELIMINAR
(B) PARA APROVAÇÃO
(C) PARA CONHECIMENTO
(D) PARA COTAÇÃO
(E) PARA CONSTRUÇÃO
(F) CONFORME COMPRADO
(G) CONFORME CONSTRUÍDO
(H) CANCELADO

CONCEITO ENGENHARIA

BEMISA

PROJETO FERROSOS BARATINHA

PROJETO EXECUTIVO
EDIFICAÇÕES DAMINISTRATIVAS
RESTAURANTE/REFEITÓRIO
ARQUITETURA
PLANTA BAIXA-LAYOUT COZINHA-ESQUADRIAS

ESCALA:	N° PROJETISTA	N° DESCR3
INDICADA	008-2023-OS02-EX-ARQ-DES-001	0623FB-00-15-9067

FORMATO: A1

CONFIGURAÇÃO DE PENAS

ESCALA	PRETO
1	0,1
2	0,2
3	0,3
4	0,4
5	0,5
6	0,6
ESC.COLORIDA	
8	0,1
9	0,1
10	0,25
20	0,25
30	0,25
40	0,25
90	0,25
74	0,25
130	0,25
170	0,25
210	0,25

A1 (594x841)

NOTAS

PARA TABELA DE LOUÇAS VERIFICAR PRANCHA COM DETALHEMENTO DE VESTIÁRIO, INDICADA NESTE EM DOCUMENTOS DE REFERÊNCIA NESTA FOLHA

ABREVIAÇÕES

DOCUMENTOS DE REFERÊNCIA

PRANCHA DETALHAMENTO DE VESTIÁRIO - 0623FB-00-15-9071